PLANO CATASTRO-REGISTRO

CCC del predio matriz: 18-02-01-01365

Fca._____ No. _____ Folio_____

Libro _____ de_____

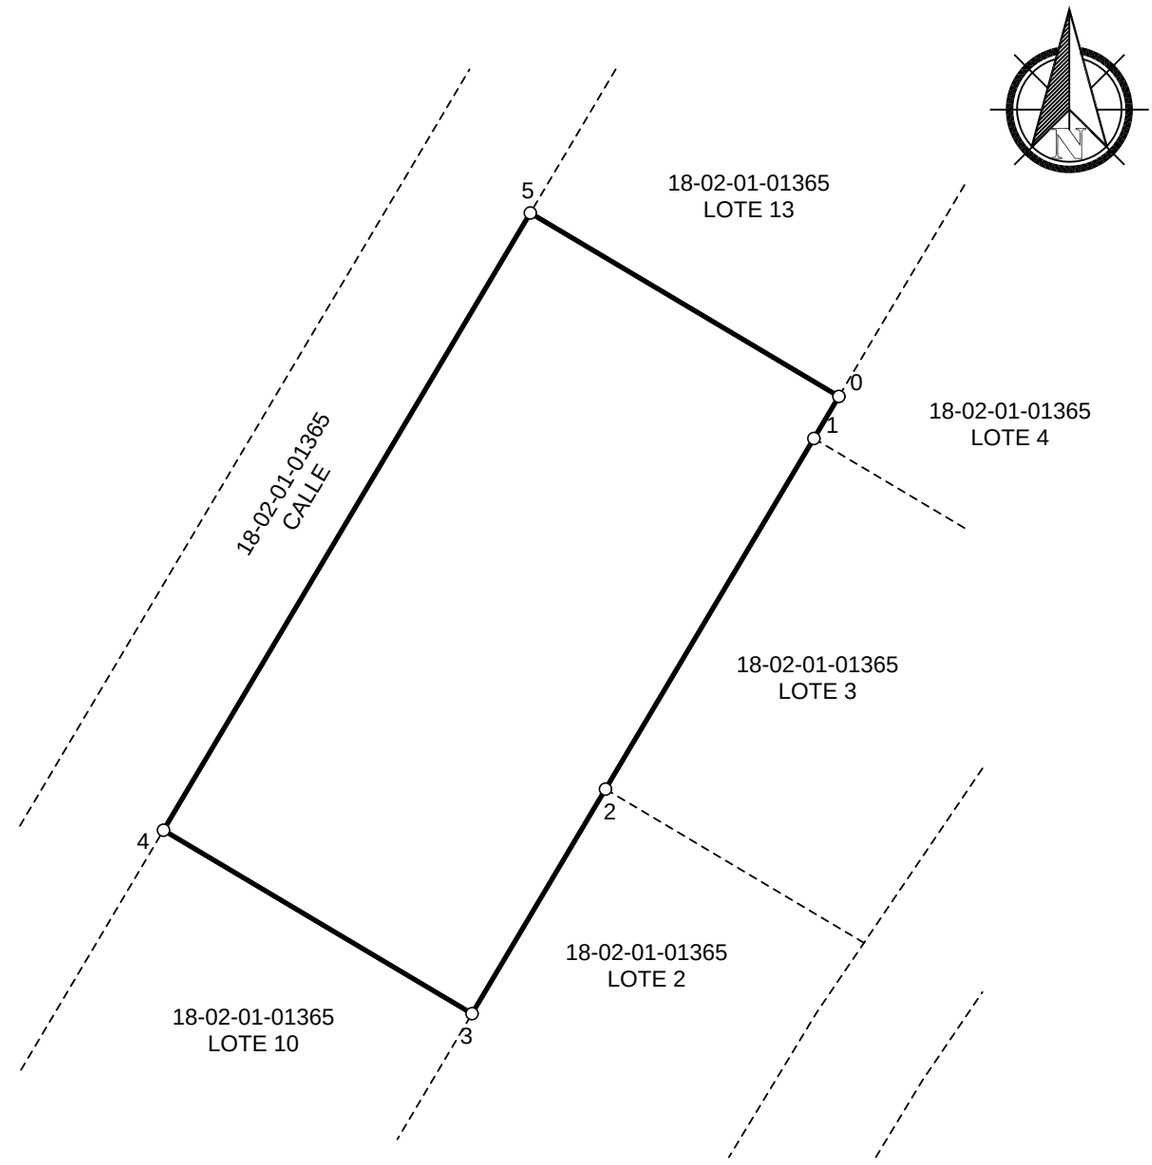

Simbología	
Vertice	○
Colindancia	- - - -
Predio	———

EST.	PO.	AZIMUTS	DIST.(m)
0	1	210° 43' 42.34"	2.72
1	2	210° 43' 42.29"	22.73
2	3	210° 43' 42.31"	14.55
3	4	300° 43' 42.33"	20.00
4	5	30° 43' 42.30"	40.00
5	0	120° 43' 42.33"	20.00

COORD. PUNTO 0 = (N: 1750254.686 E: 685387.709) GTM ZONA 15.5

PLANO DE: DESMEMBRACIÓN

FINCA: No.==========FOLIO No.==========LIBRO No.==========DE :==========

CIRCUNSCRIPCIÓN: MUNICIPIO: LIVINGSTON DEPARTAMENTO: IZABAL

DENOMINACION: Lotes 11 y 12

UBICACIÓN: BARRIO EL CACAHUATAL

OTORGANTE: ADOLFO TORIBIO GONZÁLEZ GARCÍA

ADQUIRIENTE: ALEX ADRIANA BARRIOS CARACÚN

AREA: 800.00 m^2 | ESCALA: 1/400 | FECHA: 13 de noviembre 2026

INGENIERIA, TOPOGRAFÍA, AGRIMENSURA, AGROFORESTERÍA, REGENCIA FORESTAL Y SISTEMA DE INFORMACIÓN GEOGRÁFICA -AGROFSIG-
TEL: 49028746 - 32549194

Ing. Eliazar Isaac Bó Ché,
Colegiado 8,508, - Licencia Agrimensor No. 790-PA