
PLANO CATASTRO-REGISTRO

CCC del predio matriz: _____

Fca._____ No. _____ Folio_____

Libro _____ de_____

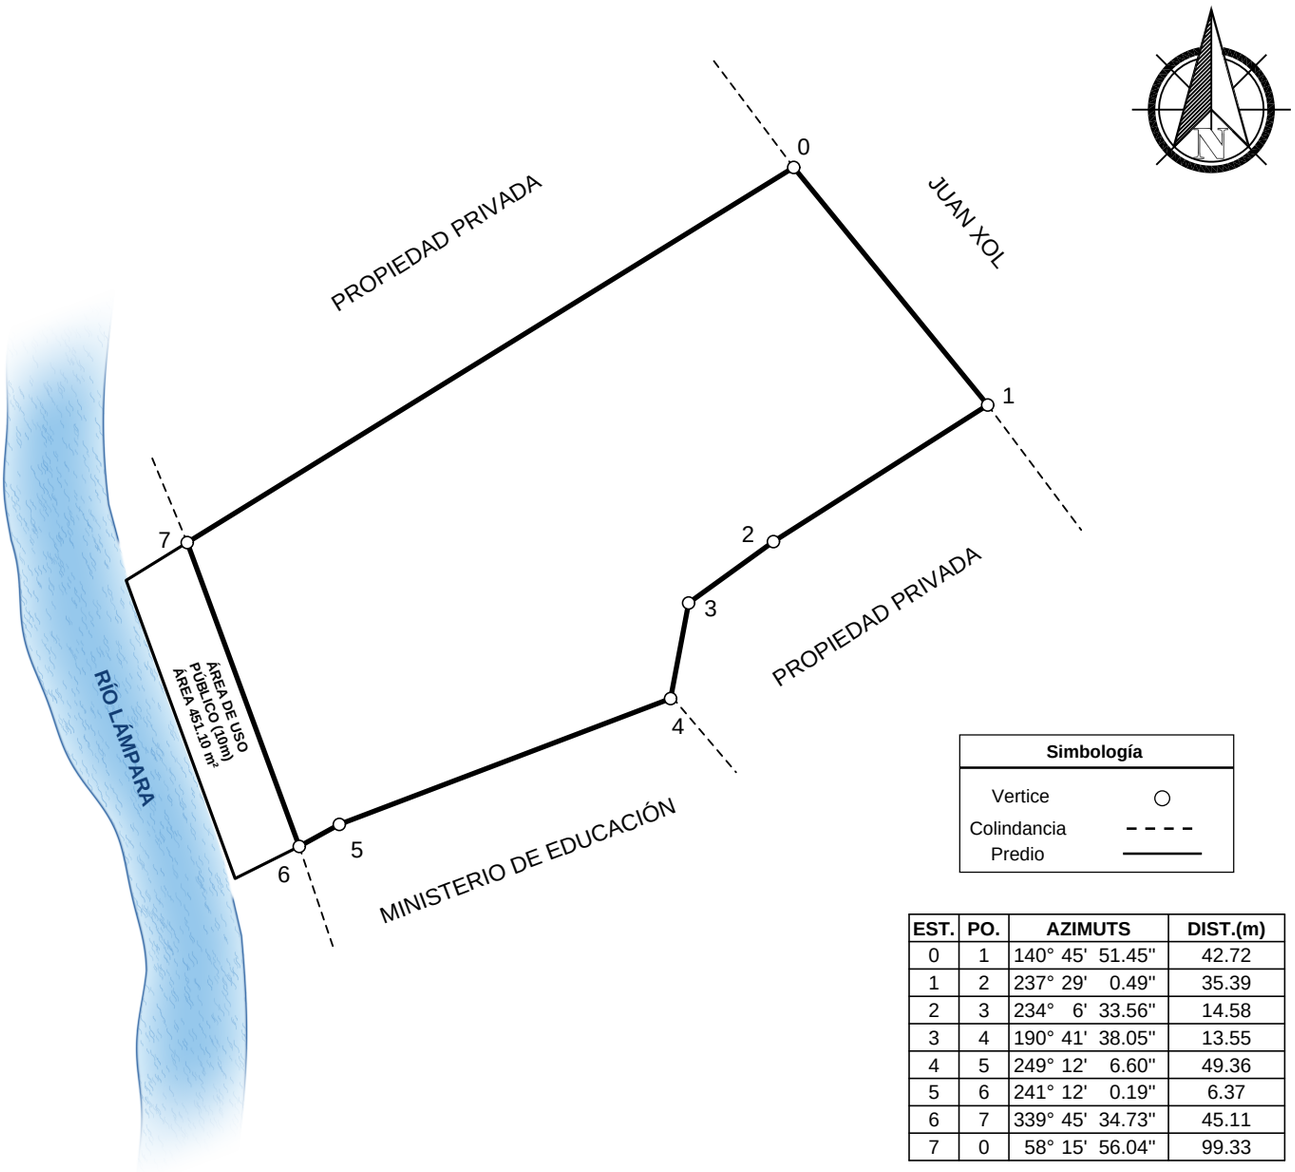

Simbología	
Vertice	○
Colindancia	- - - -
Predio	———

EST.	PO.	AZIMUTS	DIST.(m)
0	1	140° 45' 51.45"	42.72
1	2	237° 29' 0.49"	35.39
2	3	234° 6' 33.56"	14.58
3	4	190° 41' 38.05"	13.55
4	5	249° 12' 6.60"	49.36
5	6	241° 12' 0.19"	6.37
6	7	339° 45' 34.73"	45.11
7	0	58° 15' 56.04"	99.33



COORD. PUNTO 0 = (N: 1744913.905 m E: 681986.636 m) GTM ZONA 15.5
COORD. PUNTO 6 = (N: 1744819.341 m E: 681917.765 m) GTM ZONA 15.5

PLANO DE: LOCALIZACIÓN

FINCA: No.==========FOLIO No.==========LIBRO No.==========DE :==========

CIRCUNSCRIPCIÓN: MUNICIPIO: LIVINGSTON DEPARTAMENTO: IZABAL

DENOMINACION: Sin Denominación

UBICACIÓN: ALDEA BARRA LÁMPARA

OTORGANTE: EL ESTADO DE GUATEMALA

ADQUIRIENTE: AGUSTIN PAN POP, LUIS ARMANDO PAN POP y GLORIA GABRIELA PAN POP

AREA: 4,934.94 m^2 | ESCALA: 1/1000 | FECHA: 11 de noviembre 2026

INGENIERIA, TOPOGRAFÍA, AGRIMENSURA, AGROFORESTERÍA, REGENCIA FORESTAL Y SISTEMA DE INFORMACIÓN GEOGRÁFICA -AGROFSIG-
TEL: 49028746 - 32549194

Ing. Eliazar Isaac Bó Ché,
Colegiado 8,508, - Licencia Agrimensor No. 790-PA