
PLANO CATASTRO-REGISTRO

CCC del predio matriz: 18-02-01-01365

Fca._____ No. _____ Folio_____

Libro _____ de_____

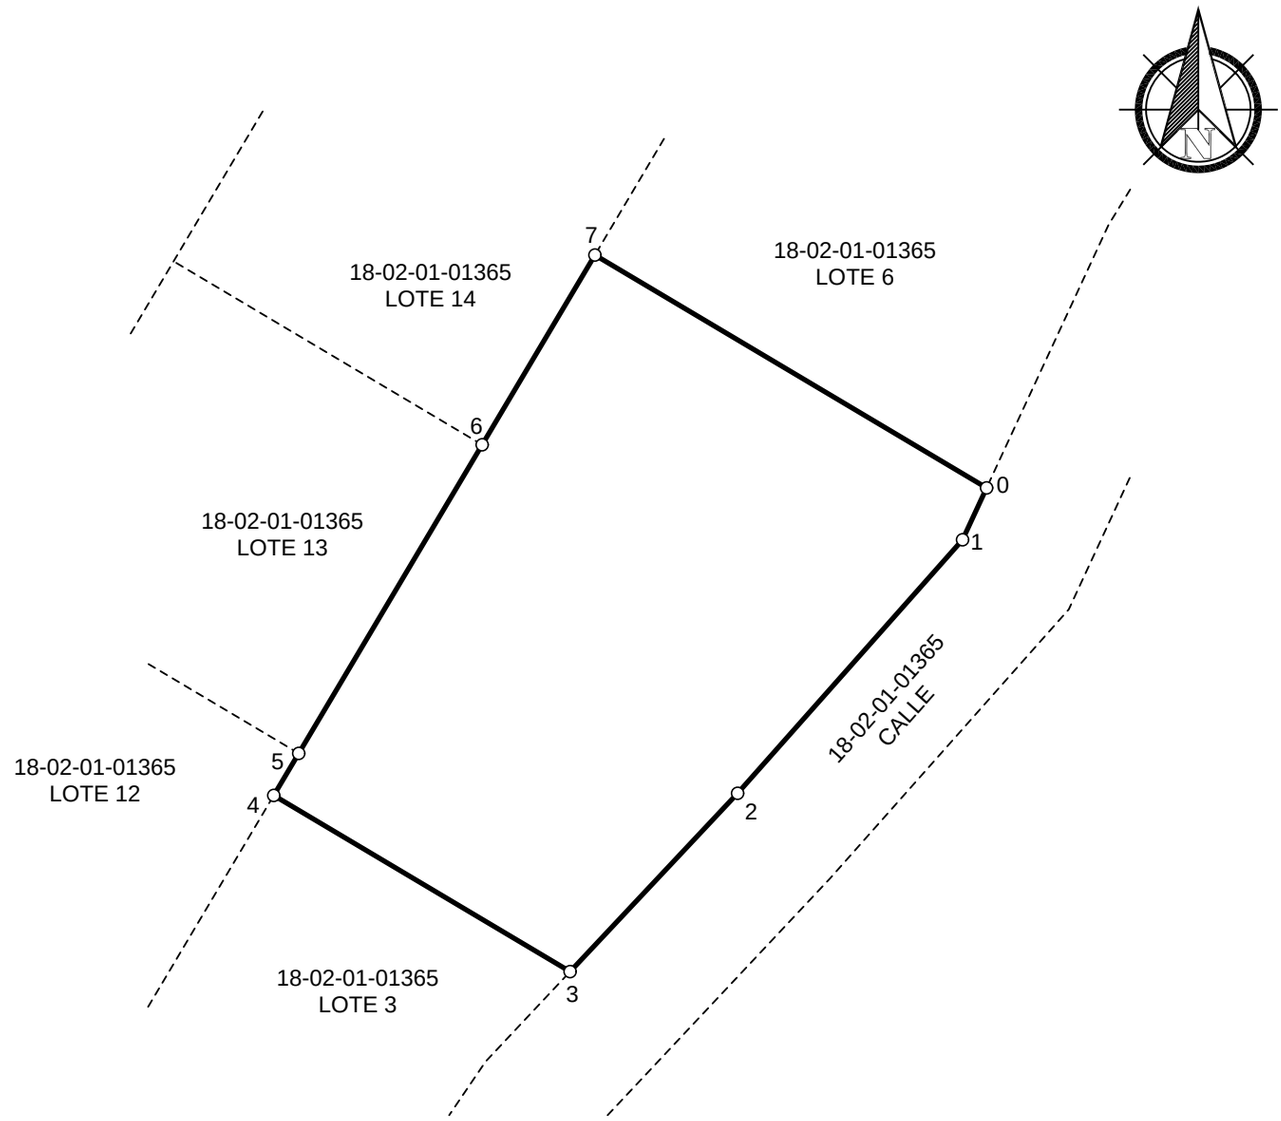

EST.	PO.	AZIMUTS	DIST.(m)
0	1	204° 52' 29.88"	3.18
1	2	221° 35' 14.39"	18.88
2	3	223° 12' 47.18"	13.63
3	4	300° 43' 42.37"	19.21
4	5	30° 43' 42.34"	2.72
5	6	30° 43' 42.30"	20.00
6	7	30° 43' 42.31"	12.30
7	0	120° 43' 42.34"	25.39

Simbología	
Vertice	○
Colindancia	- - - -
Predio	———

COORD. PUNTO 0 = (N: 1750269.475 E: 685426.034) GTM ZONA 15.5

PLANO DE: DESMEMBRACIÓN

FINCA: No.==========FOLIO No.==========LIBRO No.==========DE :==========

CIRCUNSCRIPCIÓN: MUNICIPIO: LIVINGSTON DEPARTAMENTO: IZABAL

DENOMINACION: Lotes 4 y 5

UBICACIÓN: BARRIO EL CACAHUATAL

OTORGANTE: ADOLFO TORIBIO GONZÁLEZ GARCÍA

ADQUIRIENTE: EVER ESMAILIN HERRERA CAPRIEL

AREA: 800.00 m^2 | ESCALA: 1/400 | FECHA: 11 de noviembre 2026

INGENIERIA, TOPOGRAFÍA, AGRIMENSURA,
AGROFORESTERÍA, REGENCIA FORESTAL
Y SISTEMA DE INFORMACIÓN GEOGRÁFICA
-AGROFSIG-
TEL: 49028746 - 32549194

Ing. Eliazar Isaac Bó Ché,
Colegiado 8,508, - Licencia Agrimensor No. 790-PA